
PROJECT RAN
CONSULTORIA Y CONSTRUCTORA

CUADRO DE AREAS Y PERIMETROS		
LOTE N°	AREA M2	PERIMETRO
36	100.63m²	41.10
37	100.63m²	41.10
38	100.62m²	41.10
39	115.00m²	43.40
40	115.00m²	43.40
41	115.00m²	43.40
42	143.54m²	51.55
43	120.68m²	47.73
44	128.44m²	47.64
45	103.04m²	40.80
46	103.04m²	40.80
47	103.04m²	40.80
48	90.16m²	38.50
49	90.16m²	38.50
50	90.16m²	38.50
51	90.16m²	38.50
52	90.16m²	38.50
53	90.16m²	38.50
54	90.16m²	38.50
55	90.16m²	38.50
56	90.16m²	38.50
57	90.16m²	38.50
58	90.16m²	38.50
59	85.12m²	37.60
60	85.12m²	37.60
61	85.12m²	37.60
62	85.12m²	37.60
63	97.77m²	39.91
64	129.49m²	49.71
65	111.02m²	46.40
66	105.58m²	44.64
67	140.70m²	54.22
68	137.19m²	53.22
69	133.68m²	52.21
70	126.44m²	49.97
71	267.19m²	83.27

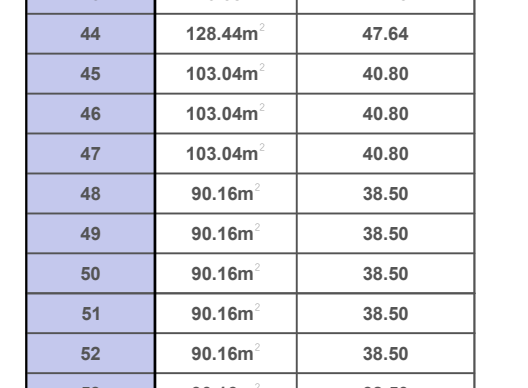


PROLG. MARISCAL CACERES 12.00 ml
seccion de via



CALLE BRASIL 9.00 ml
seccion de via



CALLE URGUAY 7.20 ml
seccion de via

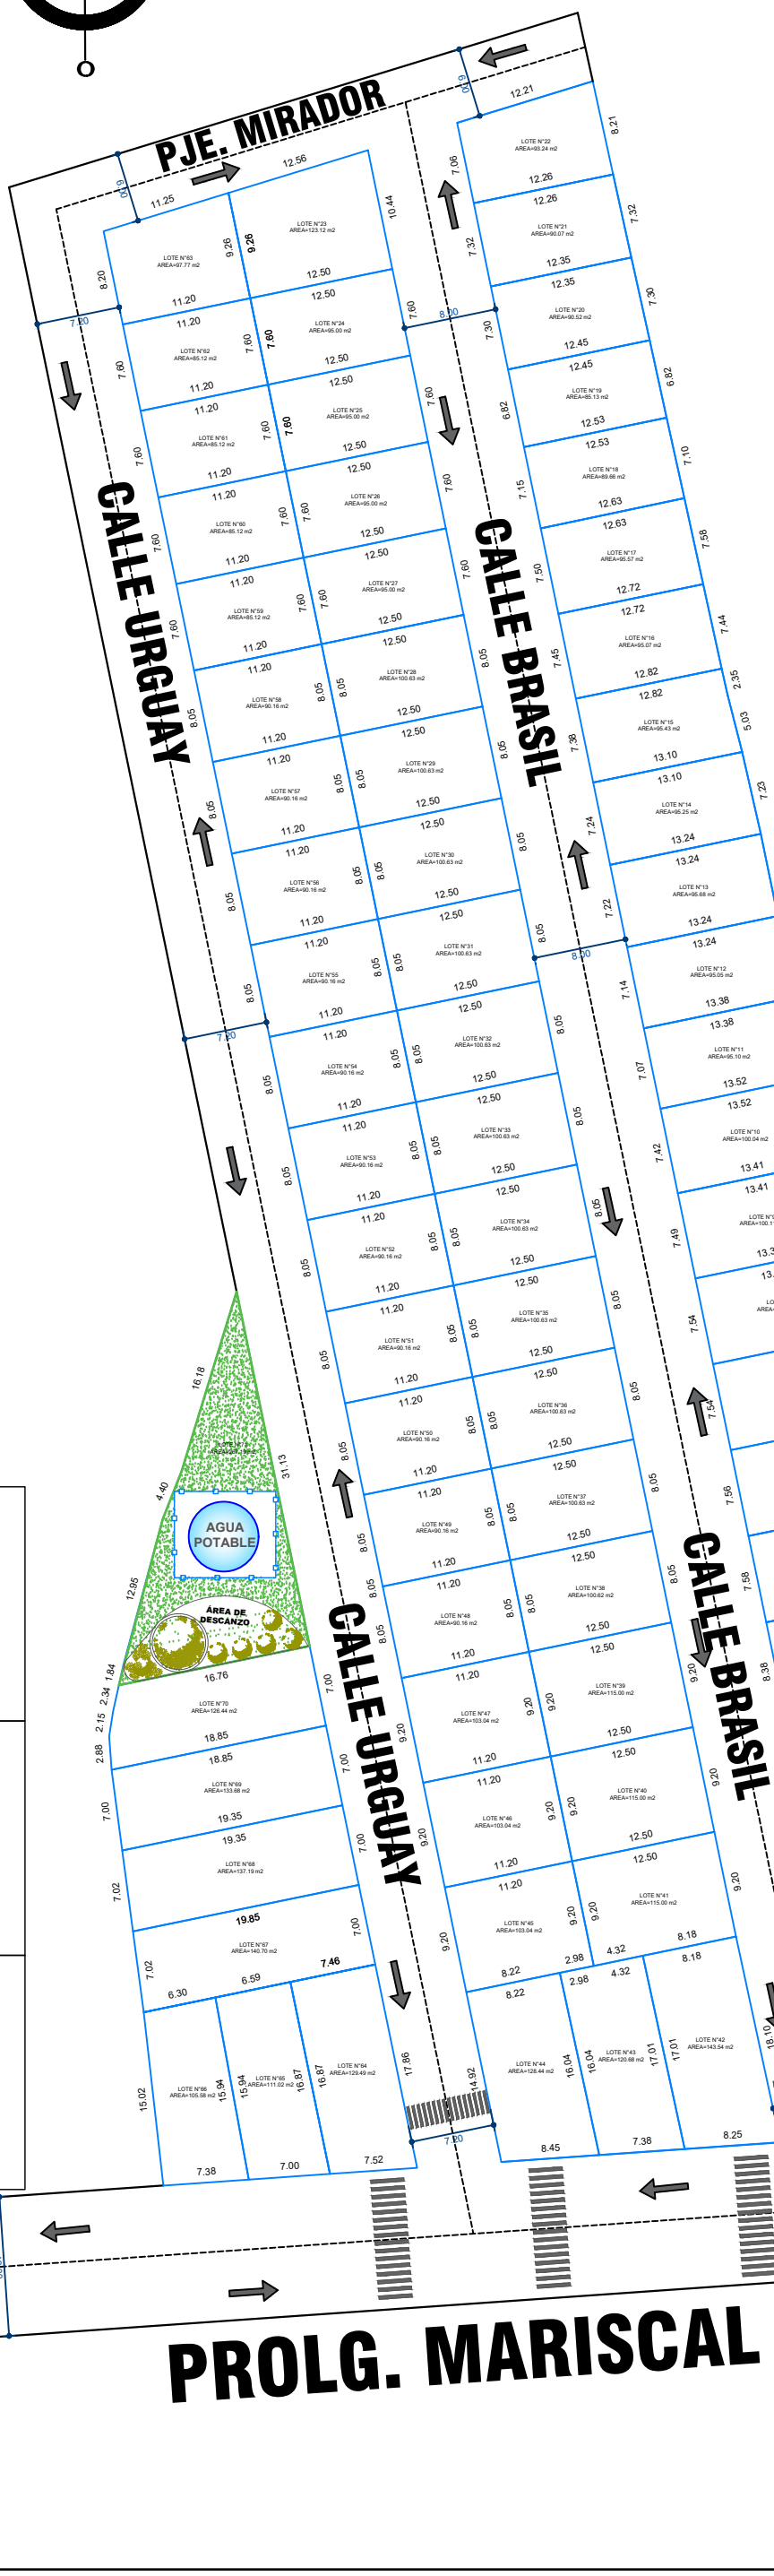

CUADRO DE AREAS Y PERIMETROS		
LOTE N°	AREA M2	PERIMETRO
1	200.00²	57.01
2	172.72m²	48.60
3	110.12m²	42.96
4	110.15m²	43.05
5	100.06m²	41.56
6	100.10m²	41.60
7	100.14m²	41.64
8	100.45m²	41.73
9	100.11m²	41.73
10	100.04m²	41.77
11	95.10m²	41.05
12	95.05m²	40.91
13	95.68m²	40.94
14	95.25m²	40.81
15	95.43m²	40.68
16	95.07m²	40.43
17	95.57m²	40.43
18	89.66m²	39.41
19	85.13m²	38.61
20	90.52m²	39.40
21	90.07m²	39.25
22	93.24m²	39.74
23	123.12m²	44.75
24	95.00m²	40.20
25	95.00m²	40.20
26	95.00m²	40.20
27	95.00m²	40.20
28	100.63m²	41.10
29	100.63m²	41.10
30	100.63m²	41.10
31	100.63m²	41.10
32	100.63m²	41.10
33	100.63m²	41.10
34	100.63m²	41.10
35	100.63m²	41.10