

CUADRO DE AREA Y PERIMETRO		
LOTE	AREA (m2)	PERIMETRO (m)
46	123.07 m2	47.83 m
47	124.15 m2	48.12 m
48	125.05 m2	48.36 m
49	126.03 m2	48.62 m
50	127.19 m2	48.88 m
51	128.01 m2	49.15 m
52	128.88 m2	49.37 m
53	129.93 m2	49.66 m
54	131.09 m2	49.97 m
55	131.80 m2	49.16 m
56	132.25 m2	50.28 m
57	133.19 m2	50.53 m
58	147.22 m2	50.73 m
59	144.55 m2	50.13 m

CUADRO DE AREA Y PERIMETRO		
LOTE	AREA (m2)	PERIMETRO (m)
16	168.75 m2	60.00 m
17	168.75 m2	60.00 m
18	168.75 m2	60.00 m
19	168.75 m2	60.00 m
20	168.75 m2	60.00 m
21	168.75 m2	60.00 m
22	168.75 m2	60.00 m
23	168.75 m2	60.00 m
24	168.75 m2	60.00 m
25	168.75 m2	60.00 m
26	168.75 m2	60.00 m
27	168.75 m2	60.00 m
28	135.29 m2	51.08 m
29	133.94 m2	50.72 m
30	132.28 m2	50.27 m
31	130.41 m2	49.78 m
32	128.80 m2	49.35 m
33	127.15 m2	48.90 m
34	168.75 m2	60.00 m
35	168.75 m2	60.00 m
36	168.75 m2	60.00 m
37	168.75 m2	60.00 m
38	168.75 m2	60.00 m
39	168.75 m2	60.00 m
40	168.75 m2	60.00 m
41	168.75 m2	60.00 m
42	168.75 m2	60.00 m
43	168.75 m2	60.00 m
44	168.75 m2	60.00 m
45	168.75 m2	60.00 m

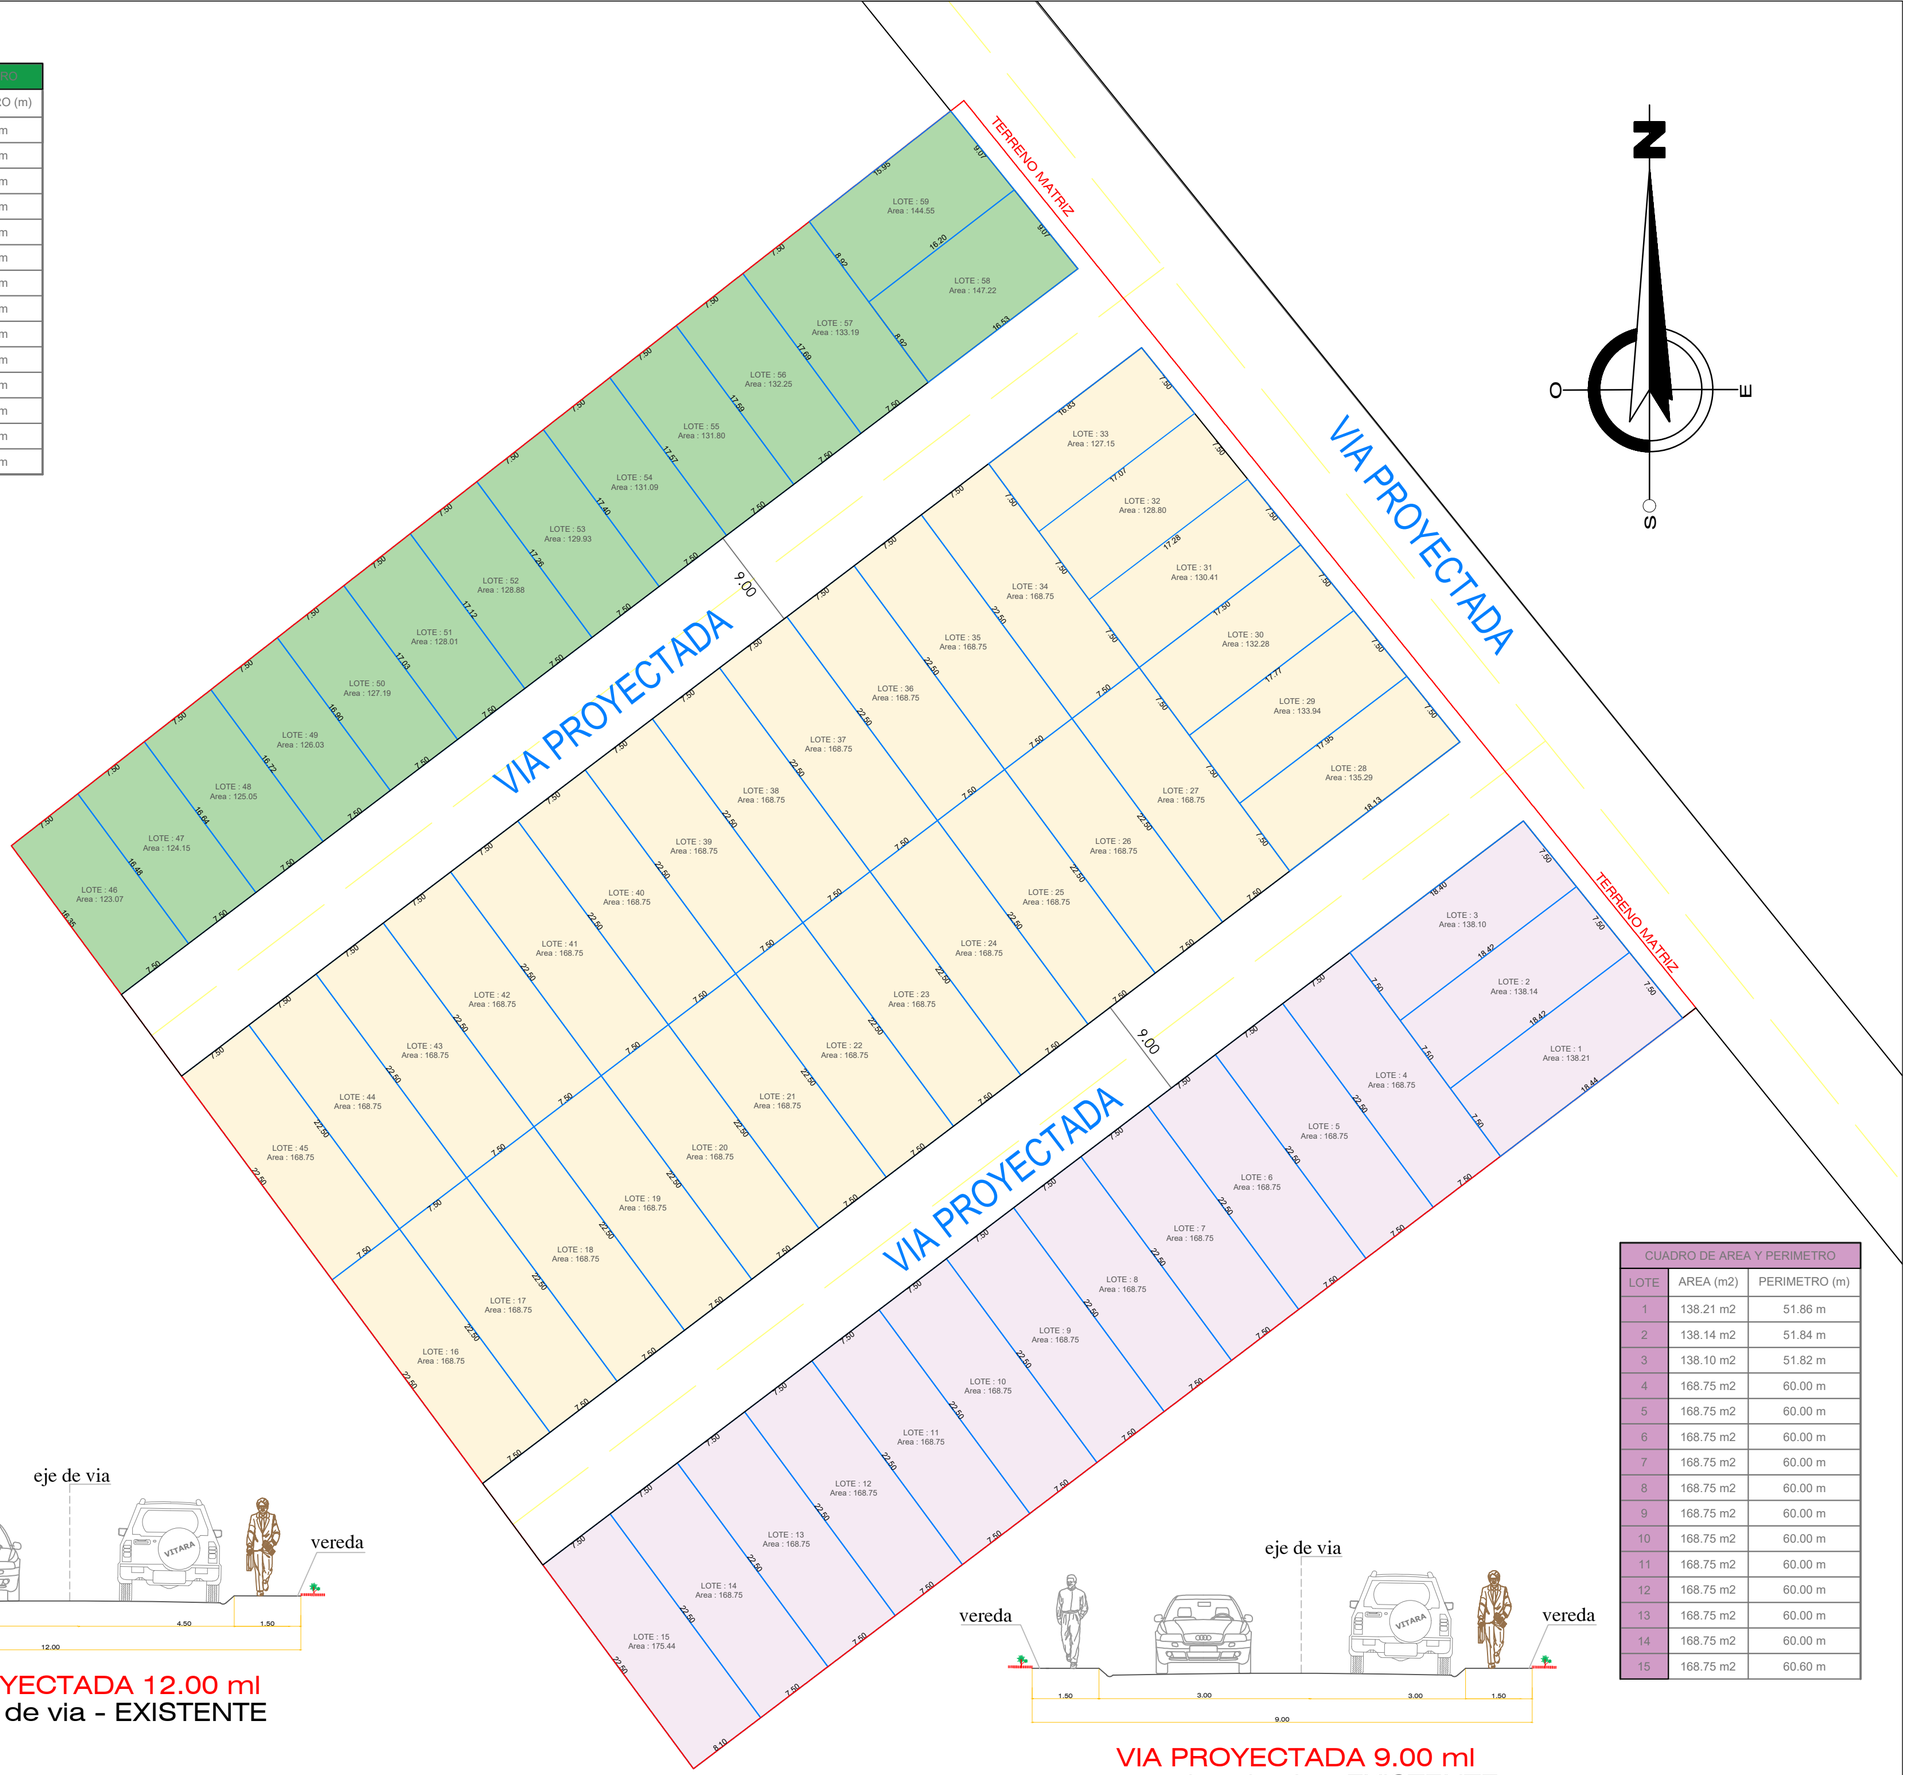

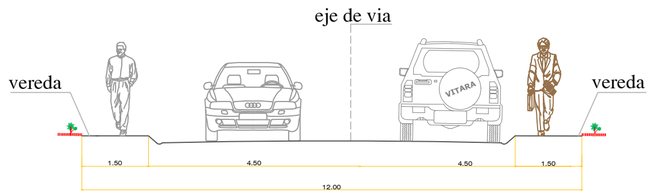

VIA PROYECTADA 12.00 ml
seccion de via - EXISTENTE

VIA PROYECTADA 9.00 ml
seccion de via - EXISTENTE

CUADRO DE AREA Y PERIMETRO		
LOTE	AREA (m2)	PERIMETRO (m)
1	138.21 m2	51.86 m
2	138.14 m2	51.84 m
3	138.10 m2	51.82 m
4	168.75 m2	60.00 m
5	168.75 m2	60.00 m
6	168.75 m2	60.00 m
7	168.75 m2	60.00 m
8	168.75 m2	60.00 m
9	168.75 m2	60.00 m
10	168.75 m2	60.00 m
11	168.75 m2	60.00 m
12	168.75 m2	60.00 m
13	168.75 m2	60.00 m
14	168.75 m2	60.00 m
15	168.75 m2	60.60 m