
URBANIZACION LA NUEVA PLANICIE

N. M.

PROJECT RAN
CONSULTORIA Y CONSTRUCTORA

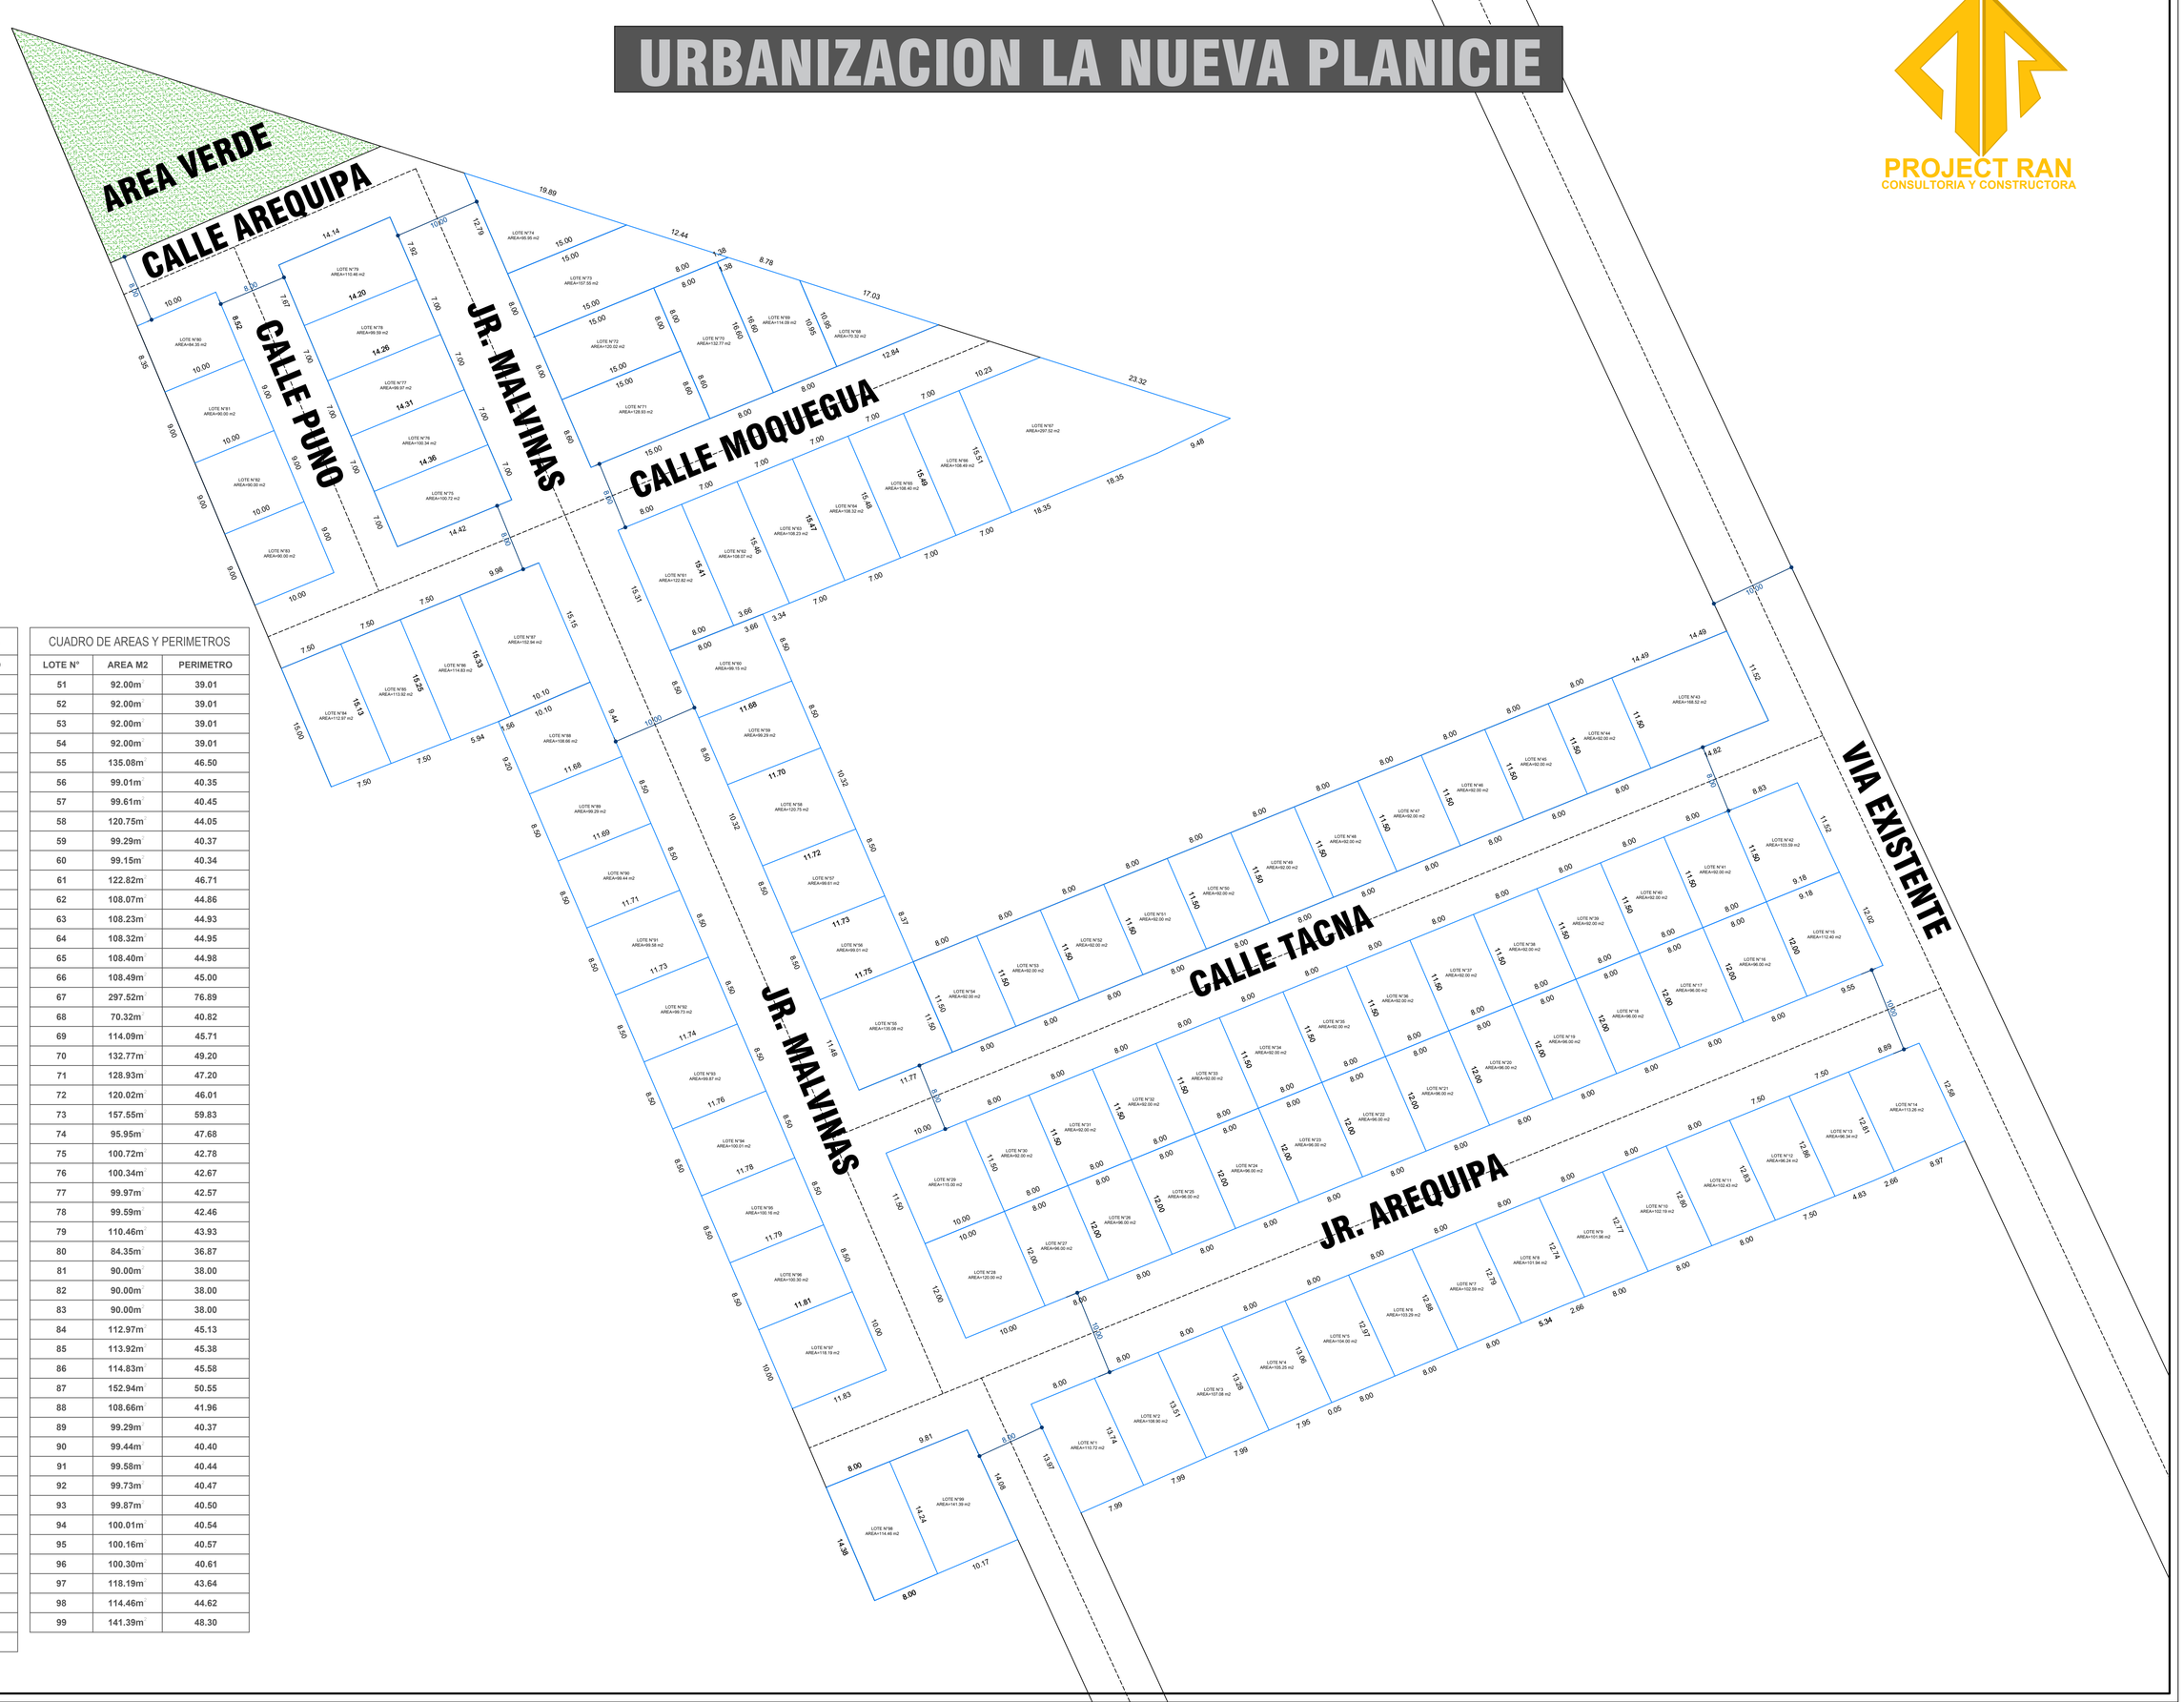

CUADRO DE AREAS Y PERIMETROS		
LOTE N°	AREA M2	PERIMETRO
1	110.72m²	43.70
2	108.90m²	43.24
3	107.08m²	42.79
4	105.25m²	42.33
5	104.00m²	42.02
6	103.29m²	41.85
7	102.59m²	41.67
8	101.94m²	41.53
9	101.96m²	41.52
10	102.19m²	41.57
11	102.43m²	41.63
12	96.24m²	40.69
13	96.34m²	40.66
14	113.26m²	43.24
15	112.40m²	42.75
16	96.00m²	40.01
17	96.00m²	40.01
18	96.00m²	40.01
19	96.00m²	40.01
20	96.00m²	40.01
21	96.00m²	40.01
22	96.00m²	40.01
23	96.00m²	40.01
24	96.00m²	40.01
25	96.00m²	40.01
26	96.00m²	40.01
27	96.00m²	40.01
28	120.00m²	44.01
29	115.00m²	43.00
30	92.00m²	39.00
31	92.00m²	39.00
32	92.00m²	39.00
33	92.00m²	39.00
34	92.00m²	39.00
35	92.00m²	39.00
36	92.00m²	39.00
37	92.00m²	39.00
38	92.00m²	39.00
39	92.00m²	39.00
40	92.00m²	39.00
41	92.00m²	39.00
42	103.59m²	41.03
43	168.52m²	52.33
44	92.00m²	39.01
45	92.00m²	39.01
46	92.00m²	39.01
47	92.00m²	39.01
48	92.00m²	39.01
49	92.00m²	39.01
50	92.00m²	39.01

CUADRO DE AREAS Y PERIMETROS		
LOTE N°	AREA M2	PERIMETRO
51	92.00m²	39.01
52	92.00m²	39.01
53	92.00m²	39.01
54	92.00m²	39.01
55	135.08m²	46.50
56	99.01m²	40.35
57	99.61m²	40.45
58	120.75m²	44.05
59	99.29m²	40.37
60	99.15m²	40.34
61	122.82m²	46.71
62	108.07m²	44.86
63	108.23m²	44.93
64	108.32m²	44.95
65	108.40m²	44.98
66	108.49m²	45.00
67	297.52m²	76.89
68	70.32m²	40.82
69	114.09m²	45.71
70	132.77m²	49.20
71	128.93m²	47.20
72	120.02m²	46.01
73	157.55m²	59.83
74	95.95m²	47.68
75	100.72m²	42.78
76	100.34m²	42.67
77	99.97m²	42.57
78	99.59m²	42.46
79	110.46m²	43.93
80	84.35m²	36.87
81	90.00m²	38.00
82	90.00m²	38.00
83	90.00m²	38.00
84	112.97m²	45.13
85	113.92m²	45.38
86	114.83m²	45.58
87	152.94m²	50.55
88	108.66m²	41.96
89	99.29m²	40.37
90	99.44m²	40.40
91	99.58m²	40.44
92	99.73m²	40.47
93	99.87m²	40.50
94	100.01m²	40.54
95	100.16m²	40.57
96	100.30m²	40.61
97	118.19m²	43.64
98	114.46m²	44.62
99	141.39m²	48.30