
N. M.

PROJECT RAN
CONSULTORIA Y CONSTRUCTORA

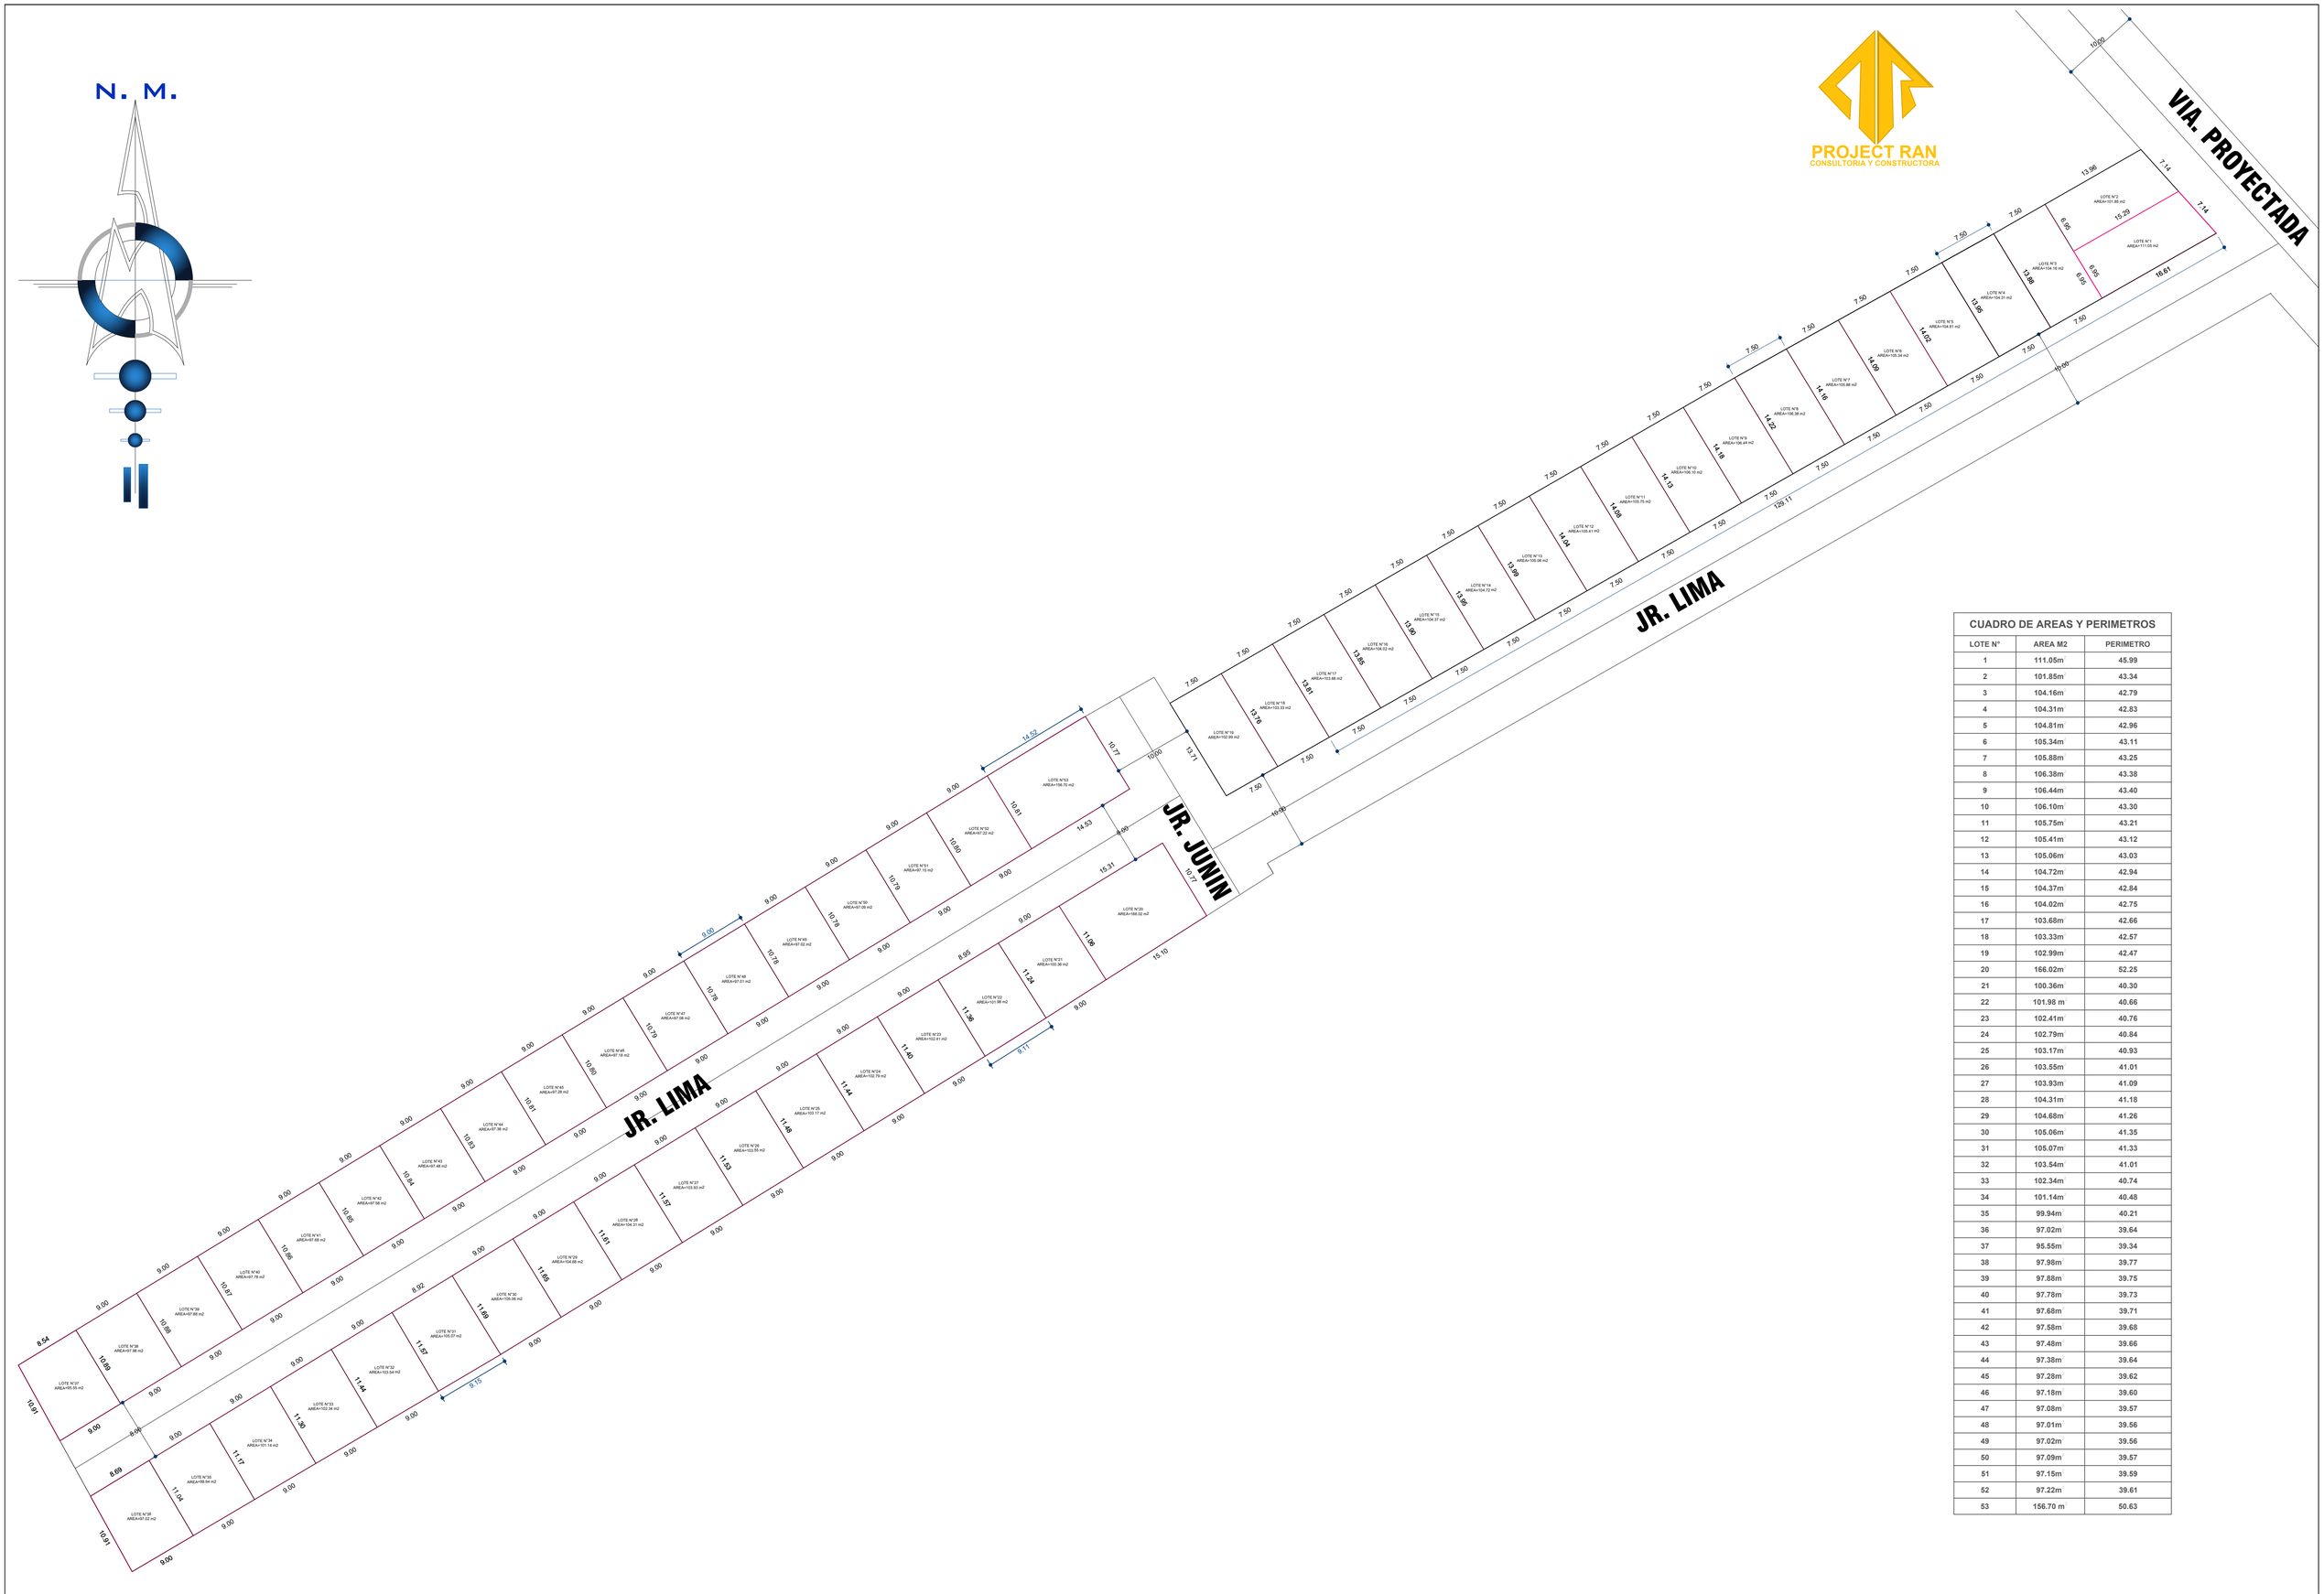

CUADRO DE AREAS Y PERIMETROS

LOTE N°	AREA M2	PERIMETRO
1	111.05m	45.99
2	101.85m	43.34
3	104.16m	42.79
4	104.31m	42.83
5	104.81m	42.96
6	105.34m	43.11
7	105.88m	43.25
8	106.38m	43.38
9	106.44m	43.40
10	106.10m	43.30
11	105.75m	43.21
12	105.41m	43.12
13	105.06m	43.03
14	104.72m	42.94
15	104.37m	42.84
16	104.02m	42.75
17	103.68m	42.66
18	103.33m	42.57
19	102.99m	42.47
20	166.02m	52.25
21	100.36m	40.30
22	101.98 m	40.66
23	102.41m	40.76
24	102.79m	40.84
25	103.17m	40.93
26	103.55m	41.01
27	103.93m	41.09
28	104.31m	41.18
29	104.68m	41.26
30	105.06m	41.35
31	105.07m	41.33
32	103.54m	41.01
33	102.34m	40.74
34	101.14m	40.48
35	99.94m	40.21
36	97.02m	39.64
37	95.55m	39.34
38	97.98m	39.77
39	97.88m	39.75
40	97.78m	39.73
41	97.68m	39.71
42	97.58m	39.68
43	97.48m	39.66
44	97.38m	39.64
45	97.28m	39.62
46	97.18m	39.60
47	97.08m	39.57
48	97.01m	39.56
49	97.02m	39.56
50	97.09m	39.57
51	97.15m	39.59
52	97.22m	39.61
53	156.70 m	50.63